



PLAN ON EAST ABUTMENT

ELEVATION ON EAST ABUTMENT

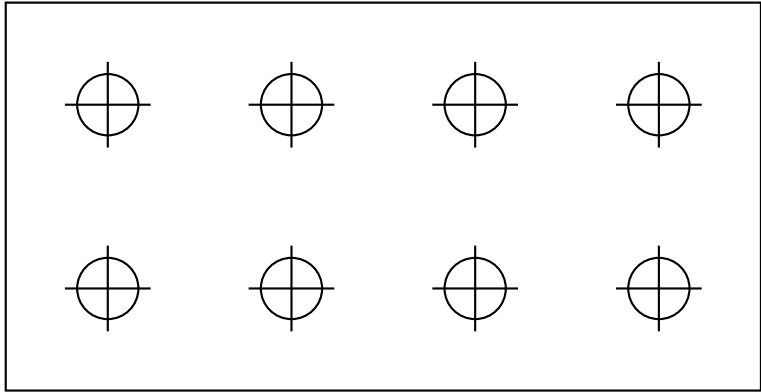

Pile cap 11.1 m x 5.7 m.

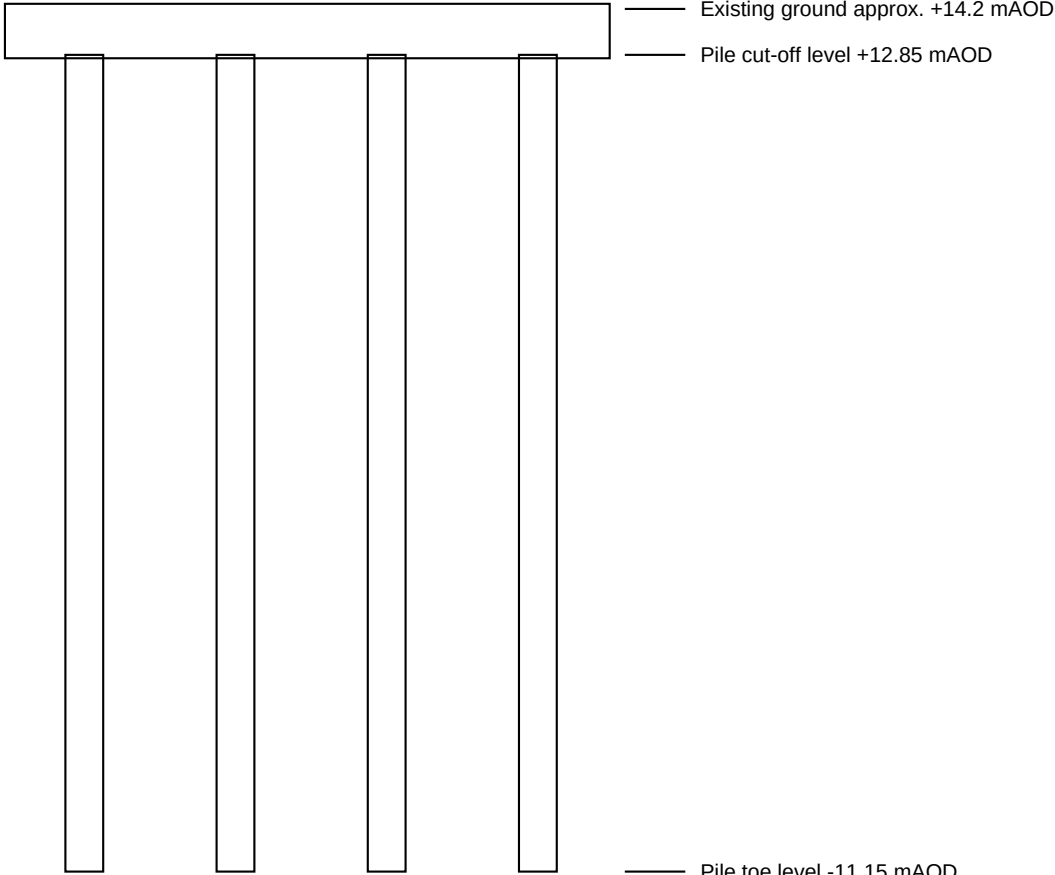

8 No. 900 mm dia. bored piles, 24.0 m long

NOTES

- 1. 8 No. 900 mm diameter bored cast-in-place piles, 24.0 m long.
- 2. Pile toe level -11.15 mAOD. Pile cut-off level +12.85 mAOD.
- 3. Piles lengthened following RFI-0012. See letter KVL-ADM-410-LT-S-0031.

Rev	Date	Description
C02	10/07/2025	Piles lengthened following RFI-0012
C01	01/03/2025	Issued for construction
P02	10/12/2024	Issued for review

Client: Northvale County Council
Designer: Arden Moss Consulting Engineers
Kestrel Valley Link Road
River Kest Bridge East Abutment General
Arrangement
Drawing number: KVL-ADM-410-DR-S-0102
Revision: C02 Status: FC - For construction
Scale: 1:100 @ A1 Date: 10 July 2025
Drawn: LC Checked: PN Approved: DO