



PLAN ON EAST ABUTMENT

ELEVATION ON EAST ABUTMENT

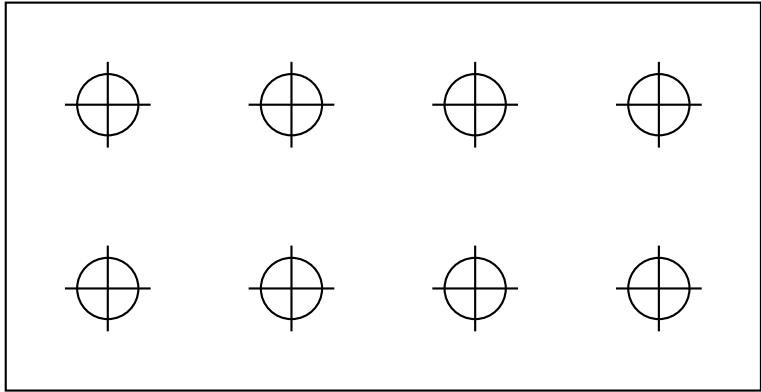

Pile cap 11.1 m x 5.7 m.

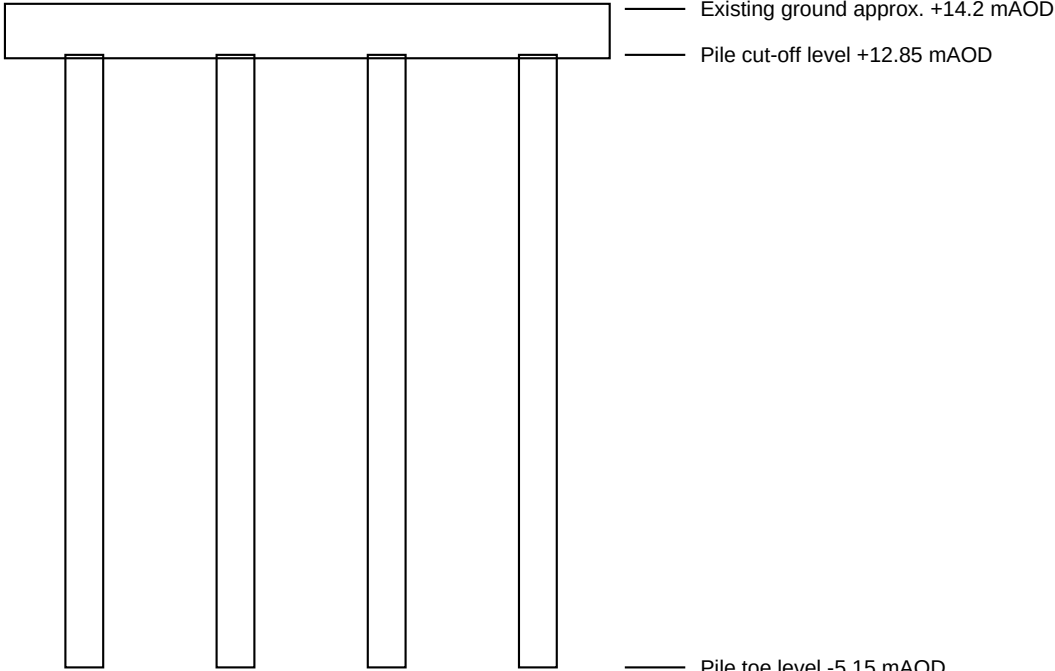

8 No. 900 mm dia. bored piles, 18.0 m long

- NOTES**
- 1. Preliminary - for review and comment only.
 - 2. Pile founding level subject to confirmation from the ground investigation.
 - 3. All levels in metres above Ordnance Datum (mAOD).

Rev	Date	Description
P02	10/12/2024	Issued for review
Client: Northvale County Council Designer: Arden Moss Consulting Engineers Kestrel Valley Link Road River Kest Bridge East Abutment General Arrangement Drawing number: KVL-ADM-410-DR-S-0102 Revision: P02 Status: RV - For review and comment Scale: 1:100 @ A1 Date: 10 December 2024 Drawn: LC Checked: PN Approved: DO		